LE CALLISTO · AGE DU 30 NOVEMBRE 2026 · LOT 6, ÉTANCHÉITÉ DES BALCONS · RÉSOLUTION 10 (BASE)

Étanchéité des balcons : ce que contient le devis

Devis SORREBA, lot 6 « Étanchéité des balcons » : 2,0 % des travaux de la base

i Bulle verte : on vous explique   ? Bulle orange : notre question pour le 19

Les 16 fiches et toutes les questions, avec leurs réponses : **cslecallisto.github.io/renovation/fiches.html**

Ce que reçoivent les balconnets

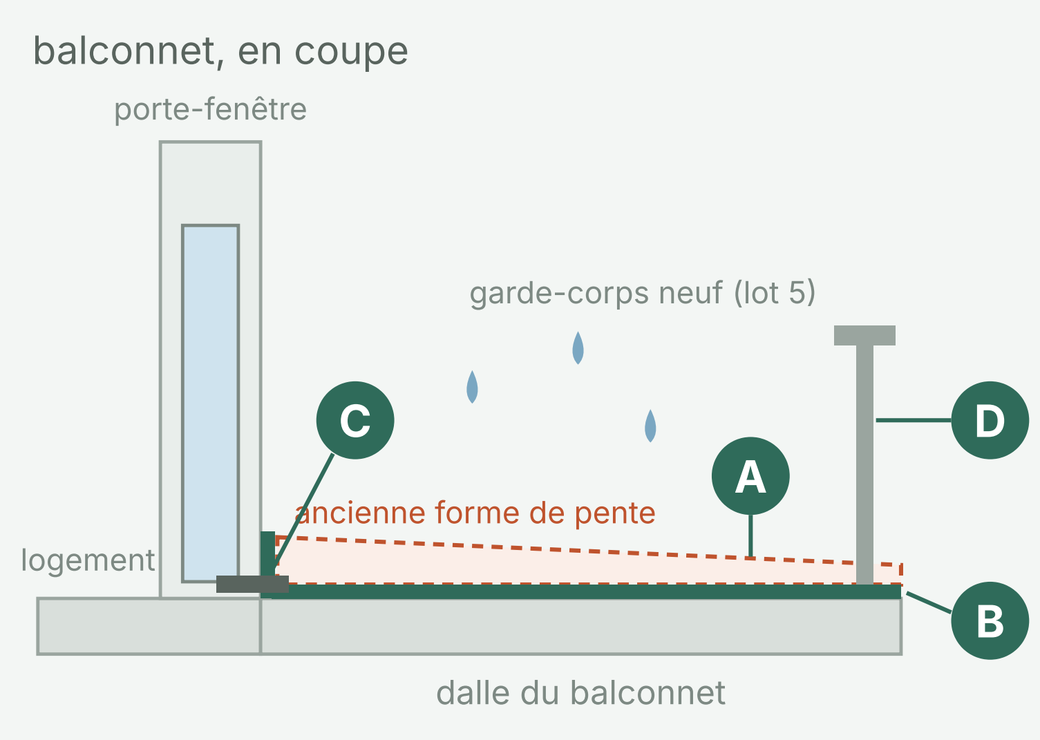

A Démolition

Les anciennes formes de pente sont démolies, puis les gravats évacués : 44,78 m² et 1,16 m³ au devis.

B Étanchéité liquide

Ponçage, puis résine en deux couches avec relevé en plinthe, sur 89,56 m² de balconnets.

i Système décrit par l'avant-projet : primaire, relevé en plinthe, équerre de renfort, deux couches de résine, silice (p. 66).

C Seuils en aluminium

Un seuil neuf devant chaque porte-fenêtre : 194,04 m, soit 2,94 m pour chacune des 66 portes-fenêtres.

D Garde-corps (lot 5)

Les garde-corps neufs se fixent sur la même dalle : les deux chantiers doivent s'enchaîner.

L05-R09.2 Pendant la même période ?

L'étanchéité des 6 loggias, avec carrelage, est chiffrée à part dans le devis, sans être soumise au vote.

Les 5 postes du devis montants hors taxes

	Poste	Montant	Part
1	**Étanchéité liquide** Résine sur les surfaces courantes des balconnets 89,56 m² × 182 € L06-R10.1 Pourquoi le double de la démolition ?	16 300 €	47,0 % du total
2	**Seuils en aluminium** Devant chaque porte-fenêtre, développé de 0,70 m environ 194,04 m × 69,80 €	13 544 €	39,0 % du total
3	**Démolition** Anciennes formes de pente 44,78 m² × 63 €	2 821 €	8,1 % du total
4	**Ponçage** Préparation des surfaces 89,56 m² × 15,80 €	1 415 €	4,1 % du total
5	**Évacuation des gravats** Ramassage et évacuation 1,164 m³ × 540 €	629 €	1,8 % du total

Total des travaux 34 708,66 € HT

Du devis au budget voté

Travaux HT	34 708,66 €
TVA 10 %	+ 3 470,87 €
Total TTC	38 179,53 €
Aléas 5 %	+ 1 908,98 €
Budget maximal voté résolution 10, aléas compris	40 088,50 €
Honoraires et assurance maîtrise d'œuvre 4,5 %, syndic 3 %, dommages-ouvrage 2,5 %, frais du syndic	+ 4 377,30 €
Tout compris	44 465,81 €
Aides estimées 22,6 % de chaque euro, comme toute la base	− 10 057,15 €
Reste à financer si tous les aléas sont consommés	34 408,66 €

i Imprimé 40 088,50 € : un centime de moins que la somme (40 088,51 €).

G.1 Négociation sous ce budget ?

À l'unité

Un balconnet tout le devis, divisé par 66	525,89 € HT 66 au devis
Étanchéité liquide résine en deux couches	182 € HT/m² 105 € pour les loggias
Seuil en aluminium devant les portes-fenêtres	69,80 € HT/m 194,04 m
Démolition anciennes formes de pente	63 € HT/m² 44,78 m²

Prix du devis, avant aléas, honoraires et aides. TVA de 10 % sur ce lot.

Ce que paie chaque lot après aides, avec la cave

Appartements, avec leur cave

APPARTEMENT	ALLÉE 61	ALLÉE 63	ALLÉE 65	ALLÉE 67
T1 · 61 t. 3 appartements	**214 €** avant aides 276 € 0,97 €/mois de prêt*	**214 €** avant aides 276 € 0,97 €/mois de prêt*	·	·
91 t. 6 appartements	·	·	·	**316 €** avant aides 409 € 1,44 €/mois de prêt*
T2 · 92 t. 7 appartements	·	·	**320 €** avant aides 414 € 1,46 €/mois de prêt*	·
96 t. 6 appartements	·	·	·	**333 €** avant aides 431 € 1,52 €/mois de prêt*
T2 grand · 102 t. 7 appartements	·	·	**354 €** avant aides 458 € 1,62 €/mois de prêt*	·
T3 · 118 t. 21 appartements	**409 €** avant aides 529 € 1,87 €/mois de prêt*	**409 €** avant aides 529 € 1,87 €/mois de prêt*	**409 €** avant aides 529 € 1,87 €/mois de prêt*	·
133 t. 1 appartement	**461 €** avant aides 596 € 2,10 €/mois de prêt*	·	·	·
T4 · 141 t. 14 appartements	**488 €** avant aides 631 € 2,23 €/mois de prêt*	**488 €** avant aides 631 € 2,23 €/mois de prêt*	·	·
T5 · 196 t. 6 appartements	·	·	·	**678 €** avant aides 876 € 3,09 €/mois de prêt*

Garages et parkings, en plus du logement

Garage 25 tantièmes (32) **86 €** avant aides 111 € · 0,40 €/mois de prêt*	**Garage** 26 tantièmes (9) **90 €** avant aides 116 € · 0,42 €/mois de prêt*	**Parking** 7 tantièmes (2) **24 €** avant aides 31 € · 0,11 €/mois de prêt*	**Parking** 12 tantièmes (2) **41 €** avant aides 53 € · 0,19 €/mois de prêt*
Parking 14 tantièmes **48 €** avant aides 62 € · 0,22 €/mois de prêt*	**Parking** 15 tantièmes (2) **52 €** avant aides 67 € · 0,24 €/mois de prêt*	**Parking** 16 tantièmes (2) **55 €** avant aides 71 € · 0,26 €/mois de prêt*	**Parking** 18 tantièmes (2) **62 €** avant aides 80 € · 0,29 €/mois de prêt*

Caves, locaux et lot atypique

Cave allée 61 (16) **3 €** avant aides 4 € · 0,02 €/mois de prêt*	**Cave** allée 63 (16) **3 €** avant aides 4 € · 0,02 €/mois de prêt*	**Cave** allée 65 (21) **3 €** avant aides 4 € · 0,02 €/mois de prêt*	**Cave** allée 67 (18) **3 €** avant aides 4 € · 0,02 €/mois de prêt*
Local 0108 allée 67, 155 tantièmes **533 €** avant aides 689 € · 2,43 €/mois de prêt*	**Local 0127** allée 67, 134 tantièmes **461 €** avant aides 596 € · 2,10 €/mois de prêt*	**Lot 0065** allée 65, 32 tantièmes **110 €** avant aides 142 € · 0,50 €/mois de prêt*	

Étanchéité des balcons : charges communes générales, garages et parkings compris. Tout compris (travaux, aléas, honoraires et assurance), clés de la convocation, aides déduites. Repérez votre appartement par ses tantièmes (appels de charges) et son allée ; il compte avec sa cave ; ajoutez votre garage ou votre parking. Entre parenthèses : le nombre de lots. * Mensualité moyenne du prêt : éco-PTZ et prêt Copro 100, plan aidé du simulateur du site (fiche F). Contrôle : les 197 lots redonnent le total de l'immeuble au centime.

Ce que le lot fait économiser

L'étanchéité des balconnets ne fait pas gagner d'énergie et ne compte pas dans le gain réglementaire : elle protège les dalles de l'eau.

Ce que le programme fait économiser sur le gaz, chaque année

	GAZ CONSOMMÉ PAR AN	GAZ ÉCONOMISÉ PAR AN	ÉCONOMIE PAR AN	BAISSE DE LA CONSOMMATION
Aujourd'hui (gaz consommé en 2025)	479 MWh	·	·	·
Avec la base	**223 MWh**	**256 MWh**	**27 613 €**	**−53,4 %**
Base et toiture	212 MWh	267 MWh	28 800 €	−55,7 %
Base et robinets	207 MWh	272 MWh	29 345 €	−56,7 %
Base et les deux options	196 MWh	283 MWh	30 532 €	−59,0 %

Pour tout l'immeuble, gaz à 108 € TTC le MWh. Par logement, avec la base : de 196 € (T1) à 629 € (T5) d'économie par an. Les travaux ensemble économisent un peu moins que la somme de chacun : le simulateur du site en tient compte. Le gain réglementaire (plus bas, 40,6 % pour la base) est un autre calcul, en énergie primaire : celui qui ouvre les aides.

Gain réglementaire, celui qui ouvre les aides : la part de chaque lot

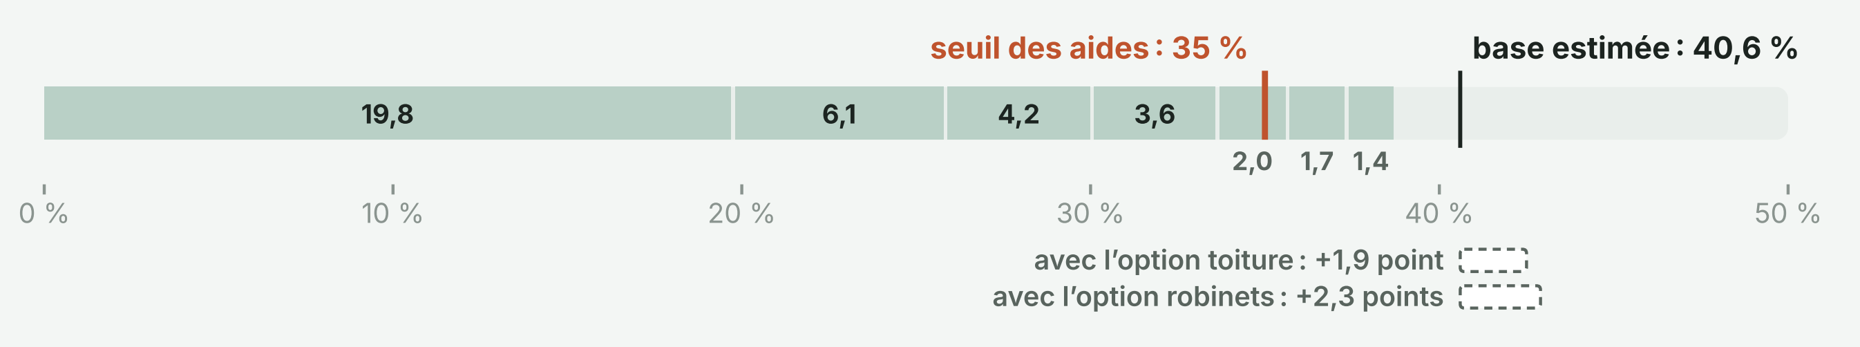

L'étanchéité des balcons ne figure pas dans ce calcul. Gain estimé de toute la base : 40,6 %, au-dessus du seuil de 35 % qui ouvre les aides. Dans la barre, chaque lot de la base, lot par lot (38,8 points en tout) ; pour toute la base, le calcul du conseil syndical donne 40,6 %. Sous l'axe, ce que chaque option ajouterait à la base, estimée seule : toiture +1,9 point et robinets +2,3 points.

À savoir

- **Répartition.** Charges communes générales (10 000 tantièmes, garages compris), comme l'écrit la résolution 10.

  G.5 Convocation ou plans ?

- **Offre de référence.** SORREBA, la moins chère des deux seules offres (ARSENAL : 47 321 € TTC). Le cabinet estimait le lot à 16 195 € TTC, 2,4 fois moins.

  L06-R10.1 D'où vient l'écart ?

- **Loggias.** L'étanchéité des 6 loggias, carrelage compris, est chiffrée à part (11 761,55 € HT), « non totalisée » : aucune résolution ne la soumet au vote.
- **Échafaudage.** Pas d'échafaudage dans ce devis : seul le lot façades en prévoit un (109 911 € HT).

  G.11 Travailler depuis celui du lot 1 ?

Nos questions pour le 19 novembre

en mots simples ; sur le site, chacune avec sa réponse

L06-R10.1 POUR LA MAÎTRISE D'ŒUVRE
Posée par le conseil syndical
Balcons : pourquoi l'offre est-elle 2,4 fois plus chère que l'estimation du cabinet, et les surfaces seront-elles vérifiées avant de signer ?

G.1 POUR LA MAÎTRISE D'ŒUVRE
Posée par le conseil syndical
Avant de signer, ferez-vous rejouer les deux meilleures offres de chaque lot pour obtenir un meilleur prix, sans dépasser le budget voté ?

G.3 POUR LA MAÎTRISE D'ŒUVRE
Posée par le conseil syndical (document du 21/10)
Quel est le planning des travaux, lot par lot, et combien de temps chaque logement sera-t-il concerné ?

G.5 POUR LE SYNDIC · RÉPONDUE
Posée par le conseil syndical (courriel au syndic)
Quelles clés de répartition s'appliquent : celles de la convocation ou celles des plans de financement ?
Réponse : Celles de la convocation. OPERENE corrige ses plans et les envoie avec l'invitation à la réunion du 19 novembre.

G.11 POUR LA MAÎTRISE D'ŒUVRE · RÉPONDUE
Posée par le conseil syndical (lecture des documents)
Seul le lot façades prévoit un échafaudage : les autres entreprises l'utiliseront-elles, et pour quelle durée de location ?
Réponse : Oui : le lot façades met son échafaudage à disposition des autres entreprises (900 € HT au forfait) ; sa durée suivra le planning (G.3).

L05-R09.2 POUR LA MAÎTRISE D'ŒUVRE
Posée par le conseil syndical (lecture des documents)
Pendant le changement des garde-corps, combien de temps les portes-fenêtres resteront-elles condamnées, et l'étanchéité du balcon sera-t-elle faite en même temps ?

Chaque question, avec sa réponse dès qu'elle est connue, est aussi sur le site : cslecallisto.github.io/renovation/fiches.html (espace des inscrits) ; dans le PDF, touchez son code ou une bulle orange. Les codes : L06-R10 = lot 6 étanchéité des balcons, résolution 10 ; L05-R09 = lot 5 serrurerie ; G = tout le programme ; H = honoraires ; F = financement. Une question de plus ? Envoyez-la au conseil syndical (groupe WhatsApp ou cslecallisto@gmail.com) : elle rejoint la liste pour le 19. Sur chaque question : à qui elle sera posée (« Pour ») et qui l'a posée (« Posée par » : le conseil syndical, ou un copropriétaire, et par quel moyen).

En images photos, schéma et plan de l'avant-projet

AUJOURD'HUI **Un balconnet.** Sol écaillé devant la porte-fenêtre (photo, p. 66).

AUJOURD'HUI **Une loggia.** Son étanchéité, chiffrée à part, n'est pas soumise au vote (photo, p. 66).

AUJOURD'HUI **Nez de dalle.** Scellement rouillé d'un ancien garde-corps (photo, p. 32).

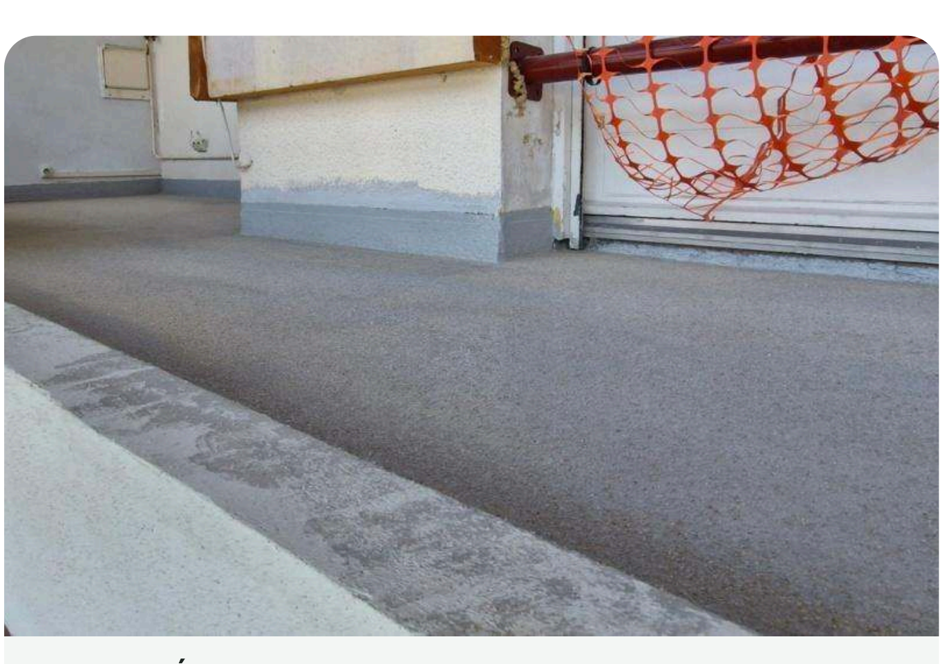

EXEMPLE **Étanchéité liquide.** Résine posée sur un autre chantier (exemple, p. 66).

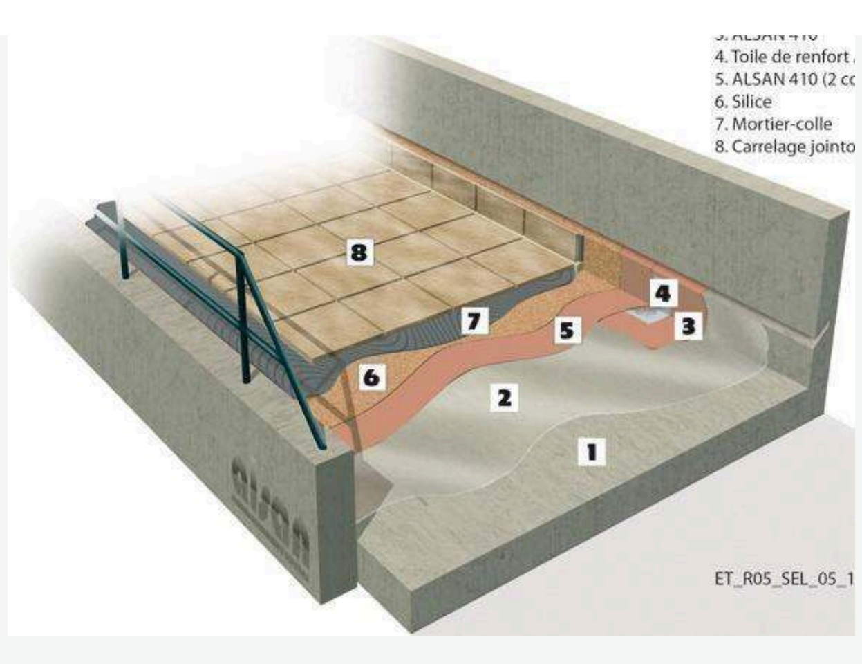

PLAN **Le système.** Primaire, relevé en plinthe, résine en deux couches, silice ; carrelage pour les loggias (schéma, p. 66).

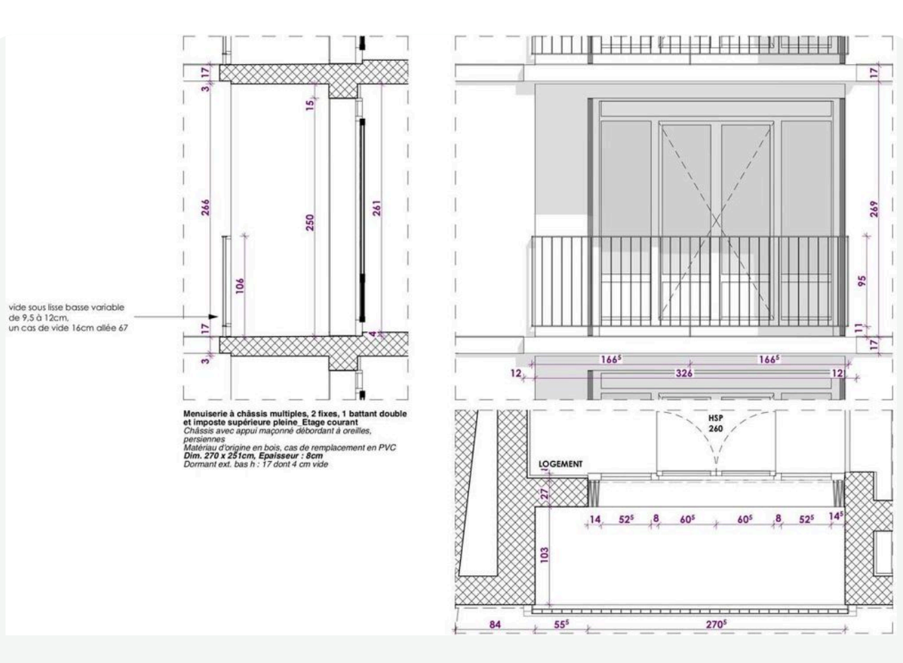

PLAN **Détail d'une loggia.** Allée 67, façade Ouest : coupe, élévation et plan (p. 32).

Images du cabinet, avant-projet du 23/04/2026 (numéros de page de l'avant-projet). Exemple : autre chantier.

Vos questions et notes à nous envoyer avant le 19

Sources : convocation à l'AGE du 30/11/2026, résolution 10 et p. 4 et 5 (aides), p. 82 à 85 du PDF (devis SORREBA : DPGF du lot 6 du cabinet Bazin renseigné par l'entreprise) ; comparatif des offres du cabinet (21/09/2026) ; avant-projet du 23/04/2026, p. 32, 66 et 125 ; simulateur du site du conseil syndical (mode convocation). Lecture du conseil syndical, 30/10/2026. Montants arrondis à l'euro.